


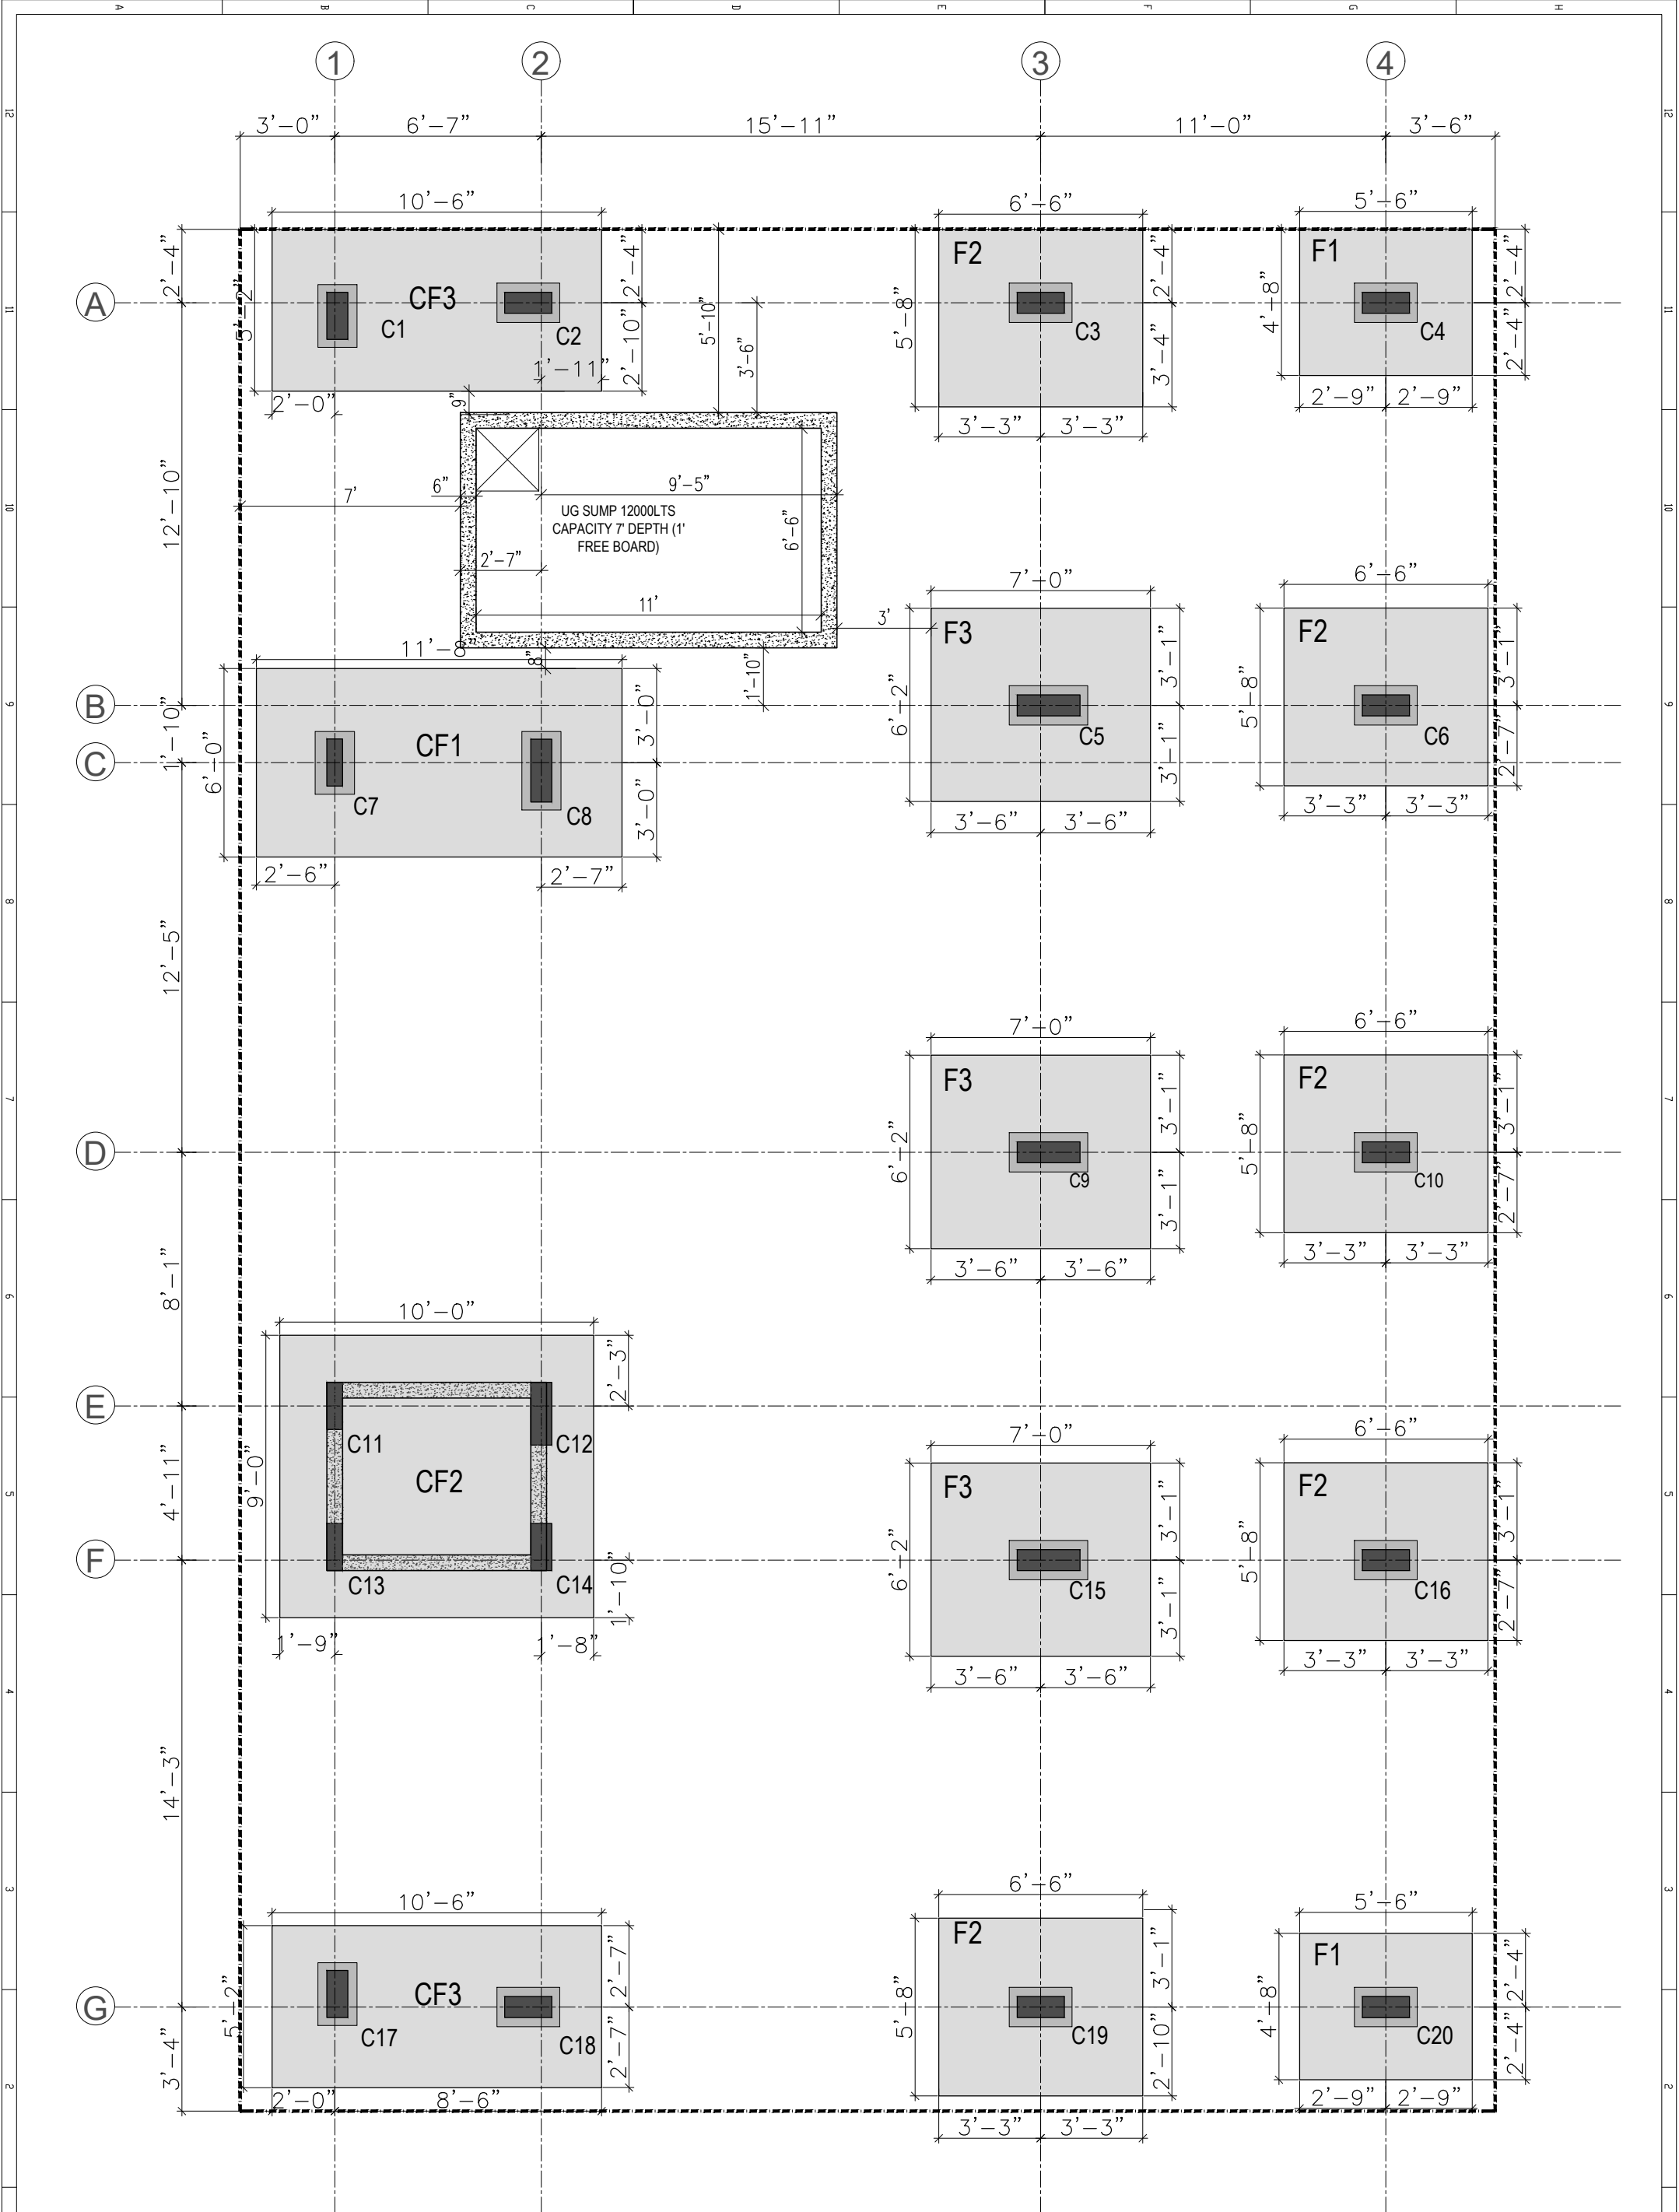

NOTES:-

1. ALL DIMENSIONS TO BE VERIFIED BEFORE EXECUTION
2. READ WITH ARCHITECTURAL DRAWINGS
3. DEPTH OF EXCAVATION 8' FROM NGL OR UPTO HARD STRATA
4. SBC OF SOIL AS PER BY SOIL TECH AT DEPTH OF 2.5M= 180KN/M2

DRAWN BY : SACHIN	
DESIGNED BY : DIVAKAR	DATE : 06.09.2026
R0	

DRAWING TITLE:
FOOTING EXCAVATION DETAILS

PROJECT:
RESIDENTIAL BUILDING FOR RAJ KUMAR, PARAMOUNT GRADENS, KANAKAPURA ROAD, BANGALORE

STRUCTURAL ENGINEER:
DIVAKAR S # 20, MSB LAYOUT, KITHAGANUR BANGALORE- 560 036