


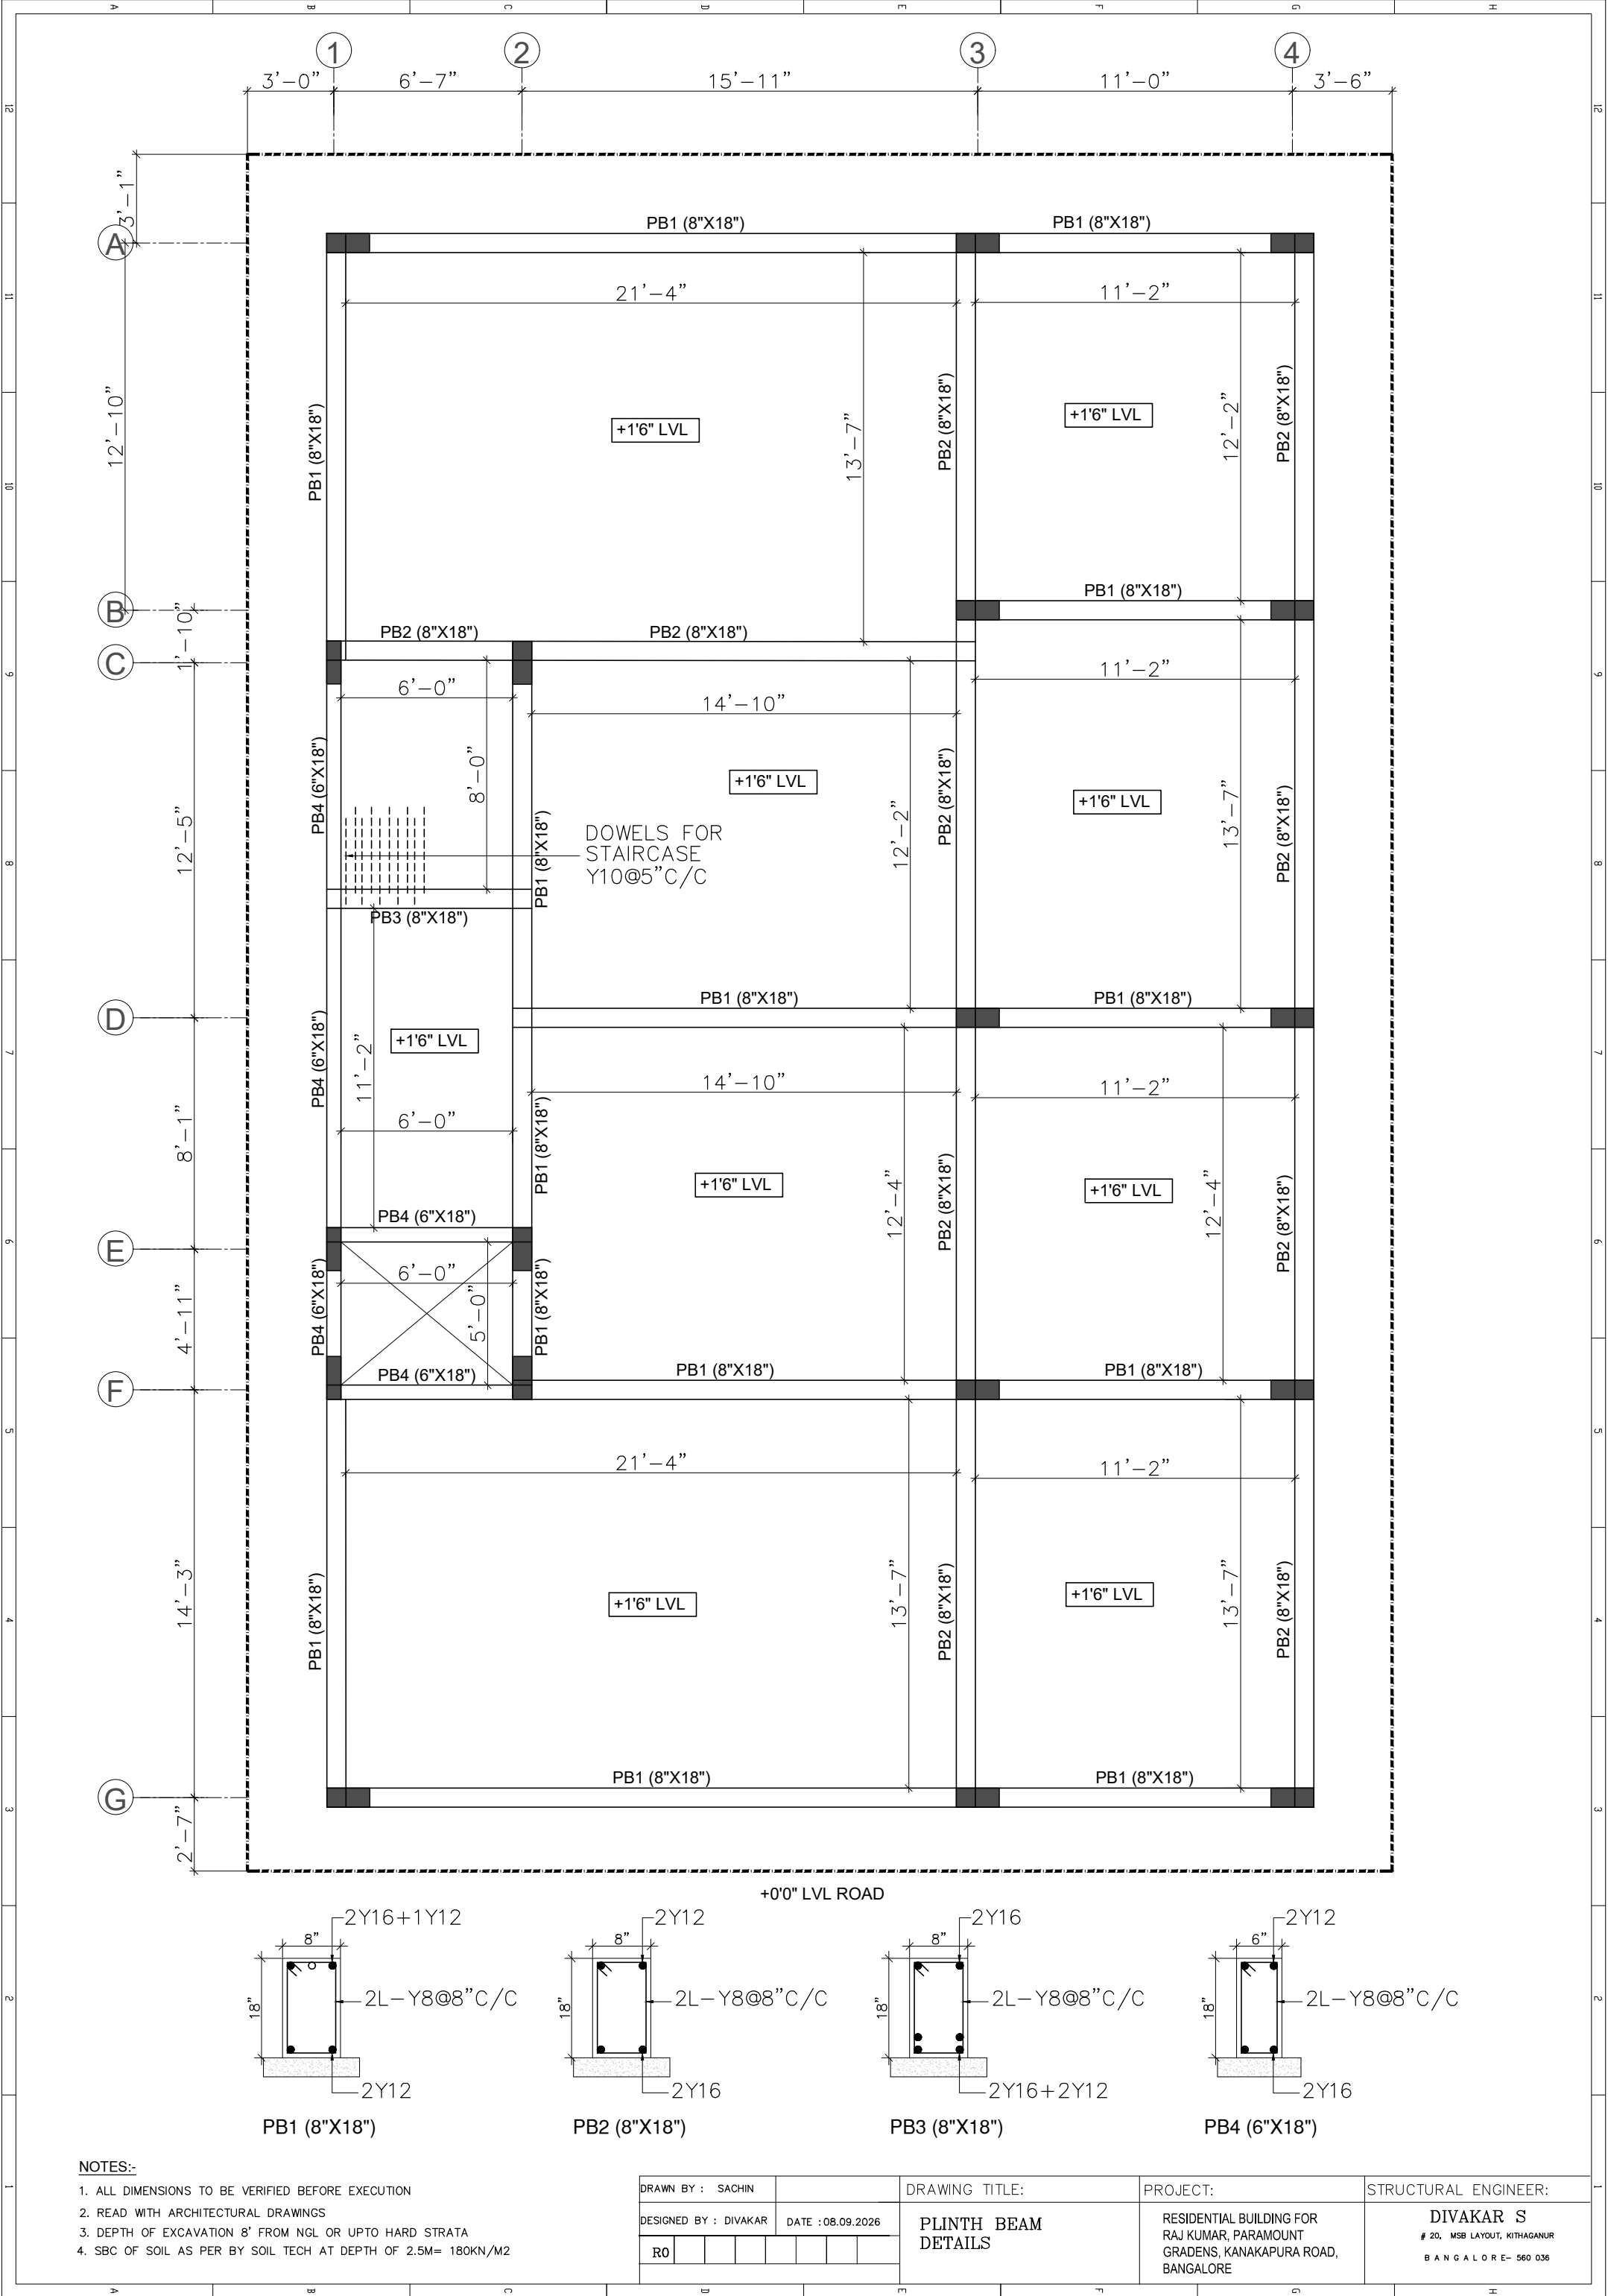

NOTES:-

1. ALL DIMENSIONS TO BE VERIFIED BEFORE EXECUTION
2. READ WITH ARCHITECTURAL DRAWINGS
3. DEPTH OF EXCAVATION 8' FROM NGL OR UPTO HARD STRATA
4. SBC OF SOIL AS PER BY SOIL TECH AT DEPTH OF 2.5M= 180KN/M2

DRAWN BY : SACHIN				DRAWING TITLE:		PROJECT:		STRUCTURAL ENGINEER:			
DESIGNED BY : DIVAKAR		DATE : 08.09.2026		PLINTH BEAM DETAILS		RESIDENTIAL BUILDING FOR RAJ KUMAR, PARAMOUNT GRADENS, KANAKAPURA ROAD, BANGALORE		DIVAKAR S # 20, MSB LAYOUT, KITHAGANUR B A N G A L O R E - 5 6 0 0 3 6			
RO											