


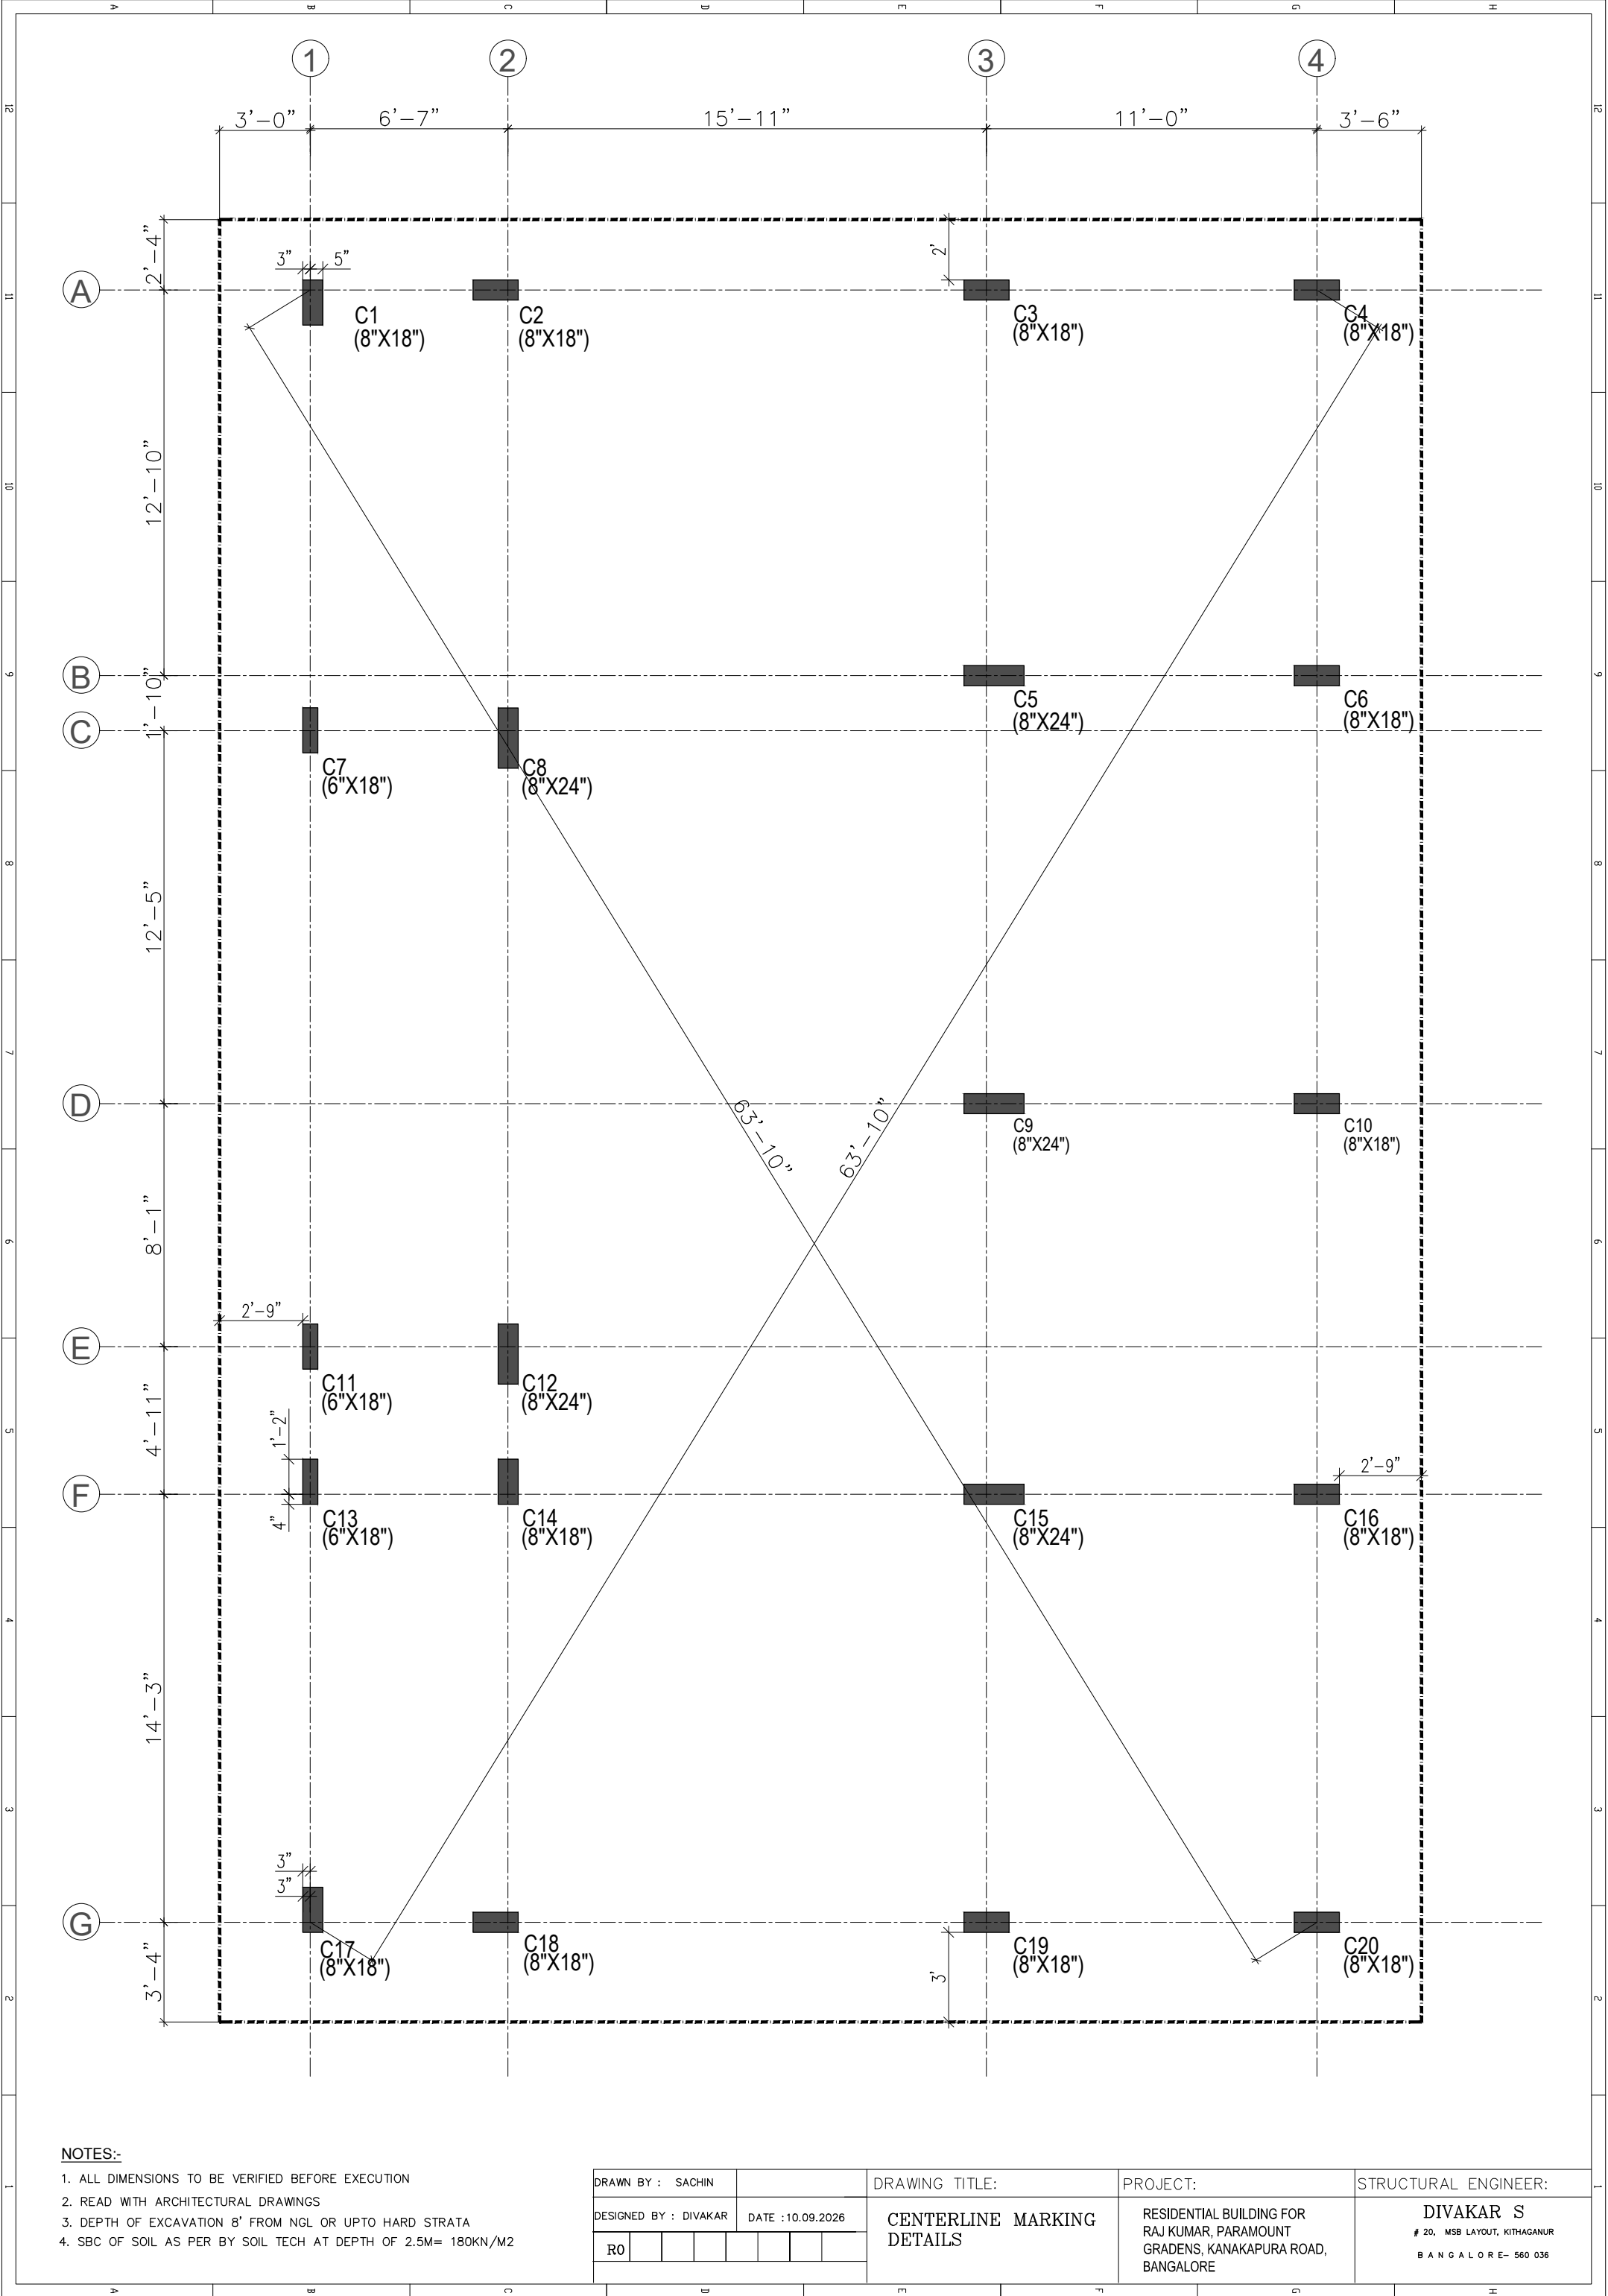

NOTES:-

1. ALL DIMENSIONS TO BE VERIFIED BEFORE EXECUTION
2. READ WITH ARCHITECTURAL DRAWINGS
3. DEPTH OF EXCAVATION 8' FROM NGL OR UPTO HARD STRATA
4. SBC OF SOIL AS PER BY SOIL TECH AT DEPTH OF 2.5M= 180KN/M2

DRAWN BY : SACHIN		DRAWING TITLE:		PROJECT:		STRUCTURAL ENGINEER:	
DESIGNED BY : DIVAKAR		DATE : 10.09.2026		CENTERLINE MARKING DETAILS		RESIDENTIAL BUILDING FOR RAJ KUMAR, PARAMOUNT GRADENS, KANAKAPURA ROAD, BANGALORE	
R0							
						DIVAKAR S # 20, MSB LAYOUT, KITHAGANUR BANGALORE- 560 036	