


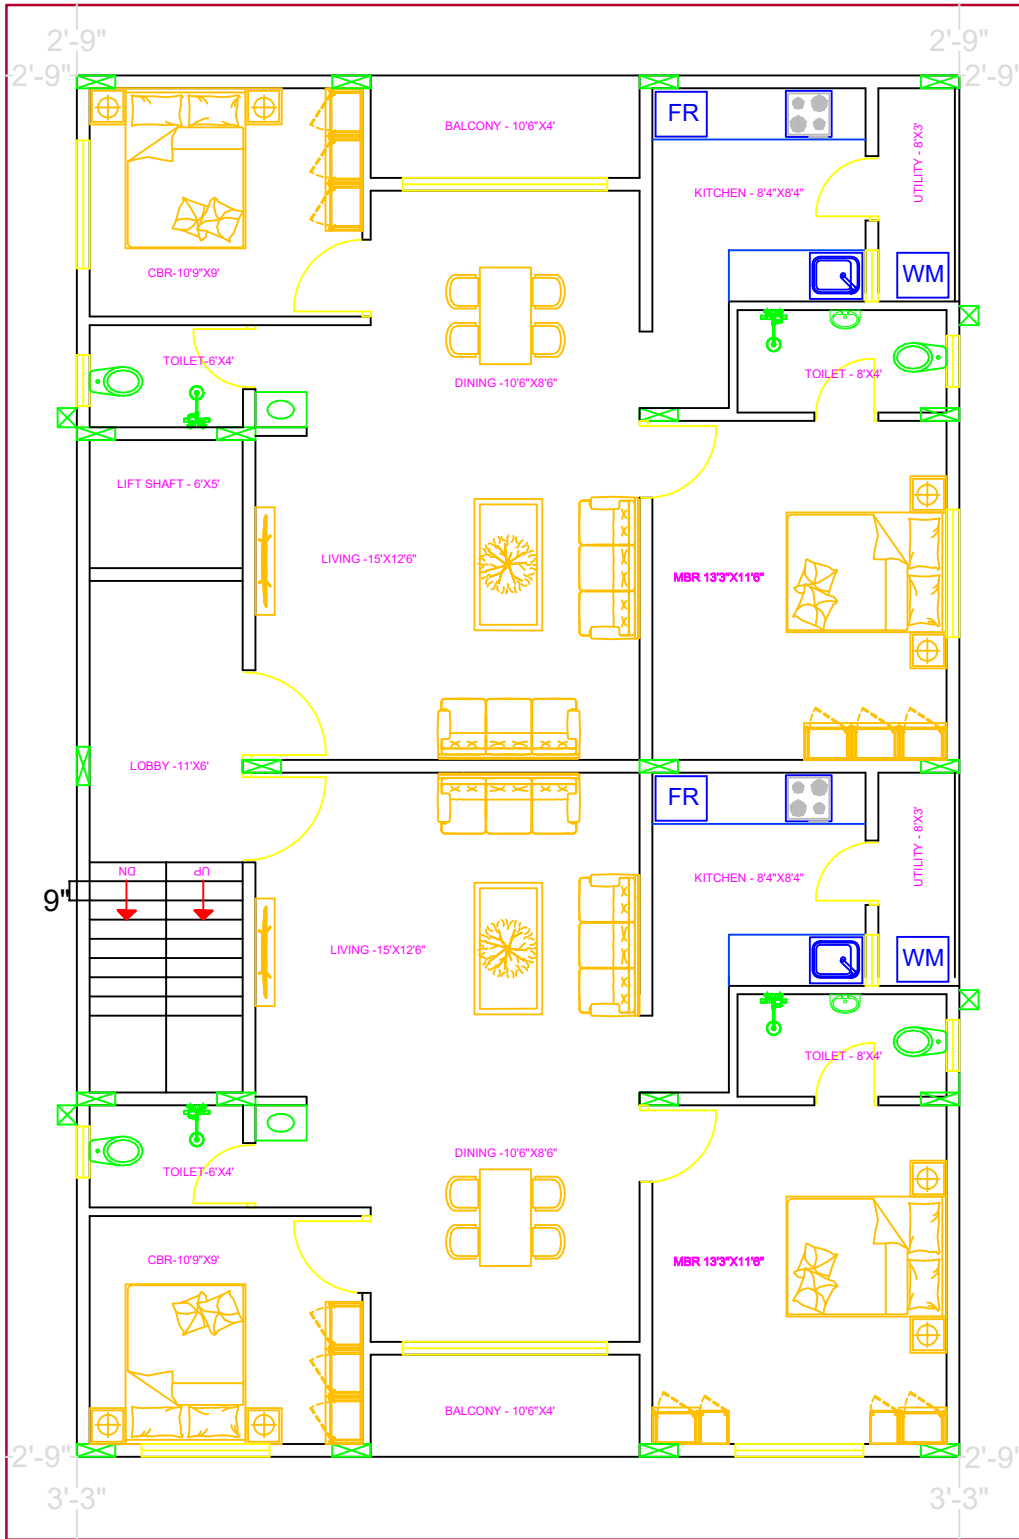


DOORS AND WINDOWS SCHUDEL				
Sno	Particular	Width(ft)	Height(ft)	nos
Door schudel				
1	Main Door	3.5	7	1
2	Bed Room Door	3	7	2
3	Toilet Doors	2.5	7	2
4	Utility	2.5	7	1
Window Schudel				
1	Living (sliding window)	8	7	1
2	Bed Room window	6	4.5	2
3	Kitchen window	3	2	1
4	Toilet ventilator	2	2	2

DRAWN BY :
M/S SRIRANGAENTERPRISES
SRINAGAR
BANGALORE
MOB : 9902465868

FIRST & SECOND FLOOR PLAN

CLINT NAME : RAJ KUMAR
#37, Paramount Gardens
Kanakapura road, Bengaluru

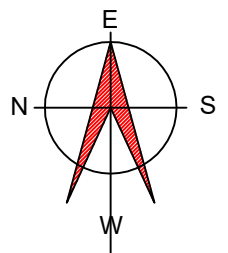

R-1

Date : 22/08/2026

NTS