


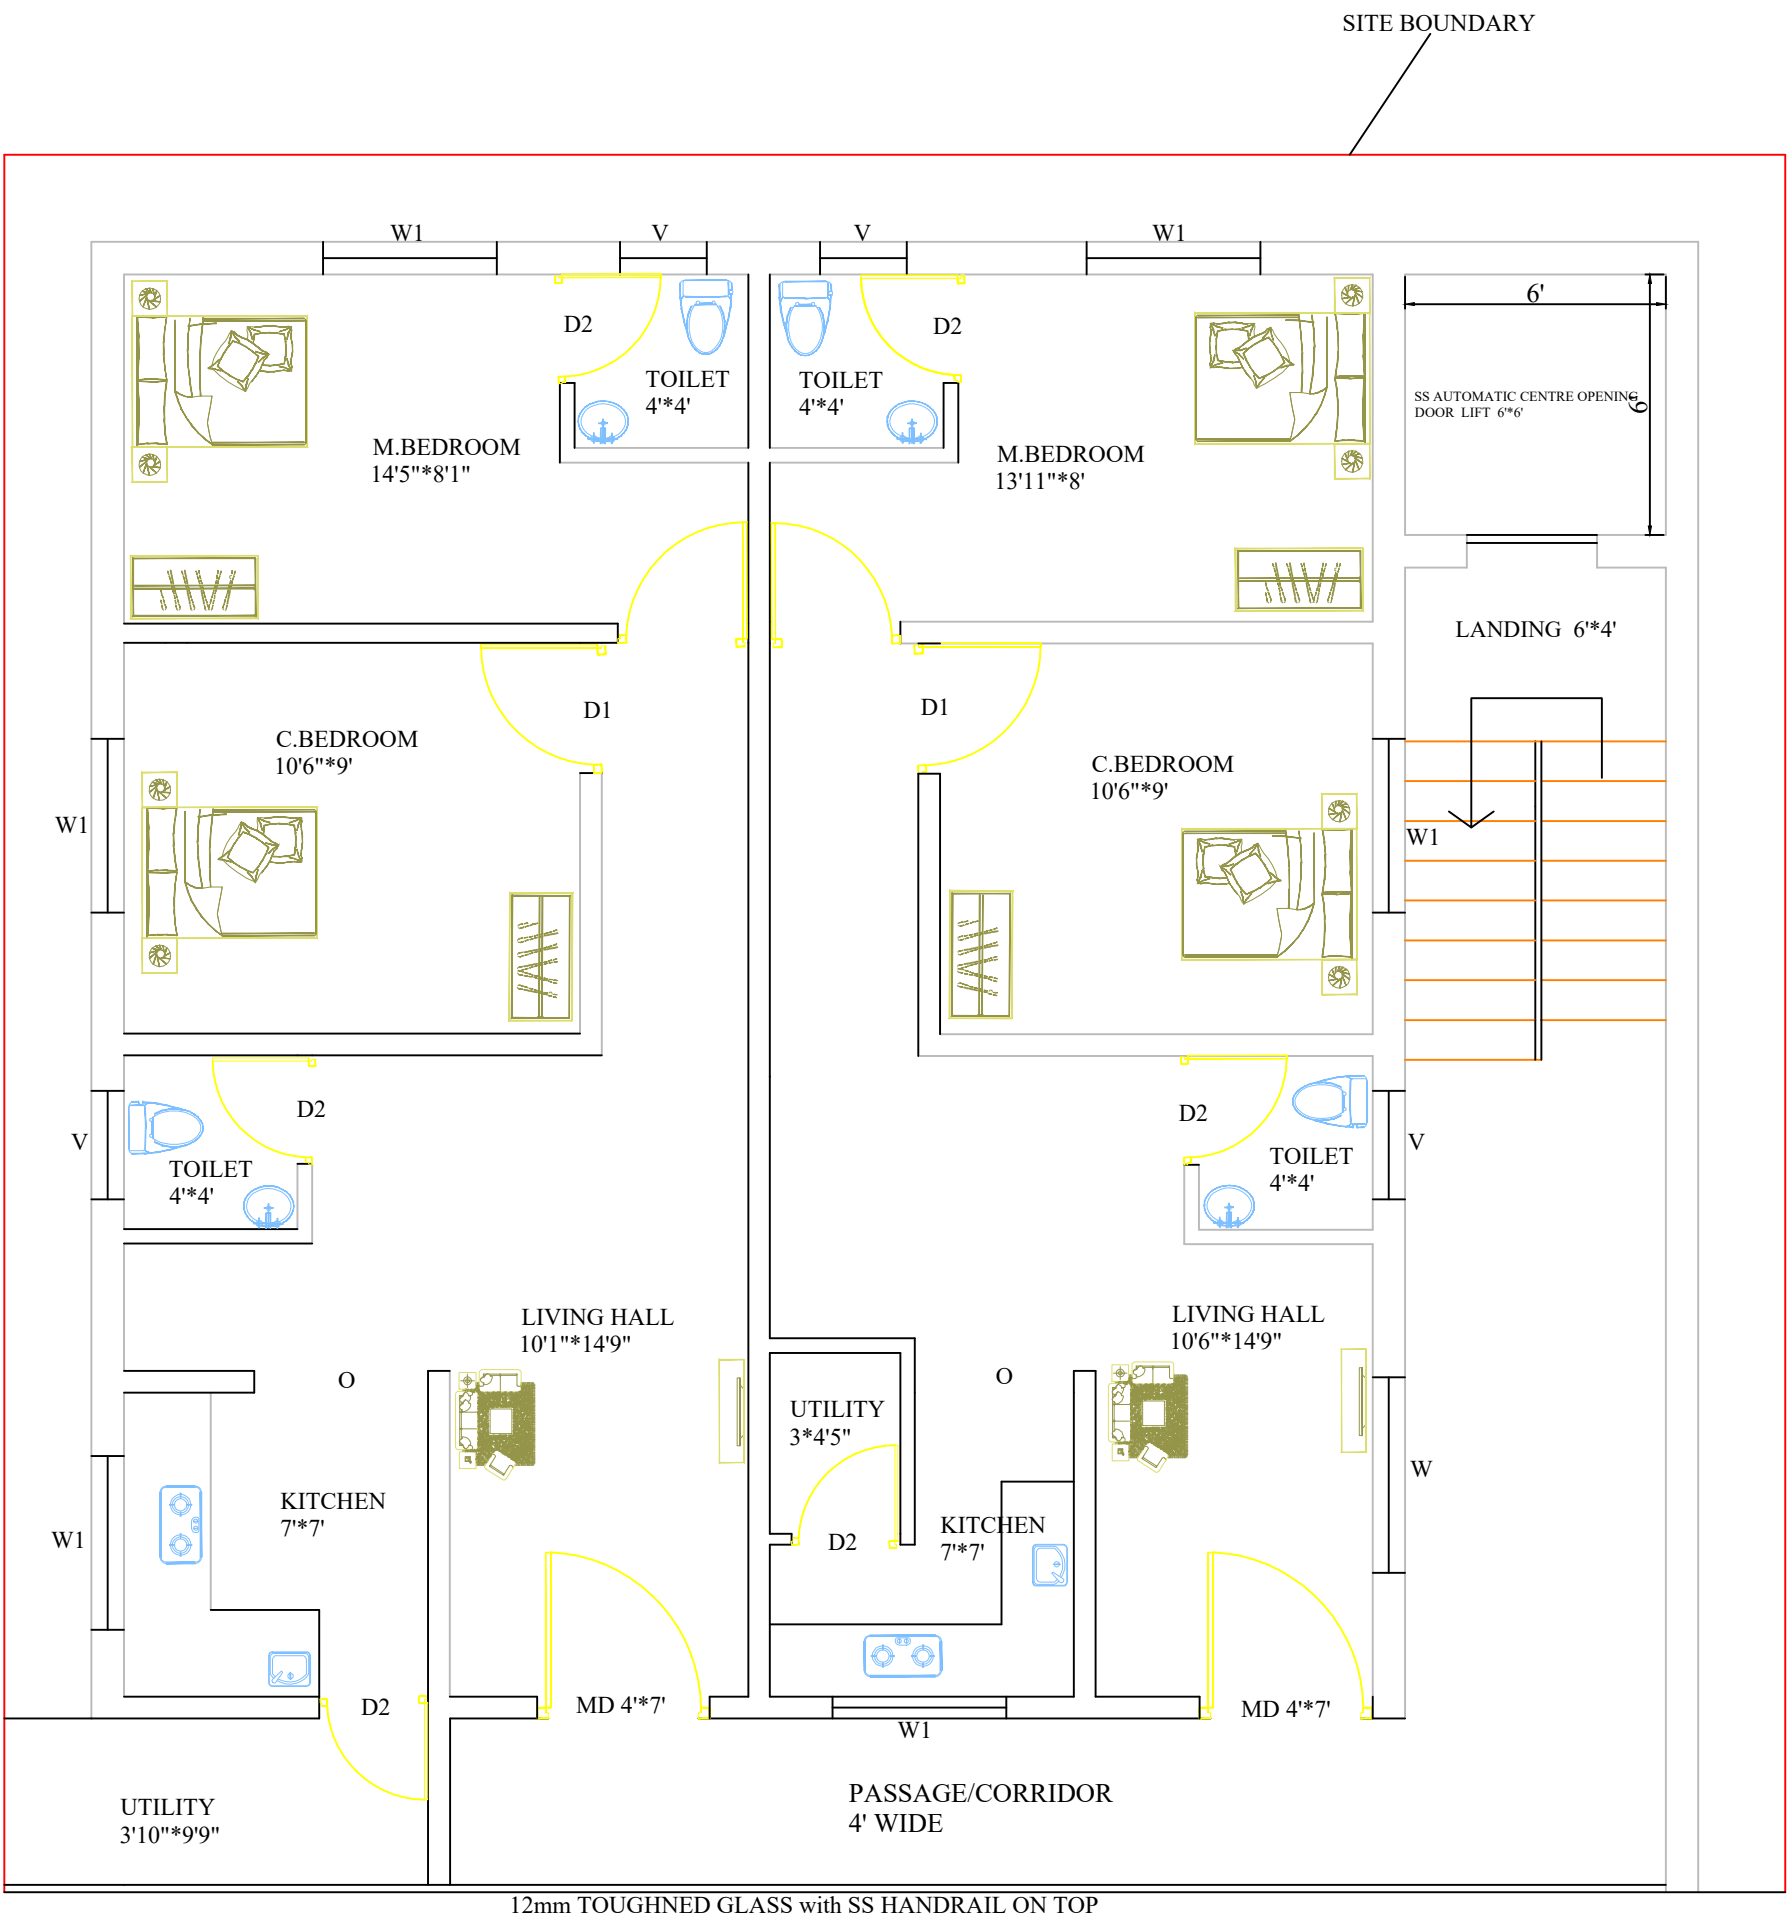


NOTE:ALL DIMENSIONS IN FEET & INCHES

OM CONSTRUCTIONS & ENGINEERING CONSULTANTS

CLIENT:MR.IMRAN PASHA,CHANDRALAYOUT,BENGALURU

SCHEDULE OF OPENINGS	
LIVING,BEDROOM,KITCHEN WALL THICKNESS	6"
TOILET,UTILITY ROOM WALL THICKNESS	4"
D1	3"7'
D2	2'6"7'
W	4'6"4'
W1	4"4'
V	2"2'
O	4"7'

**AREA: TOTAL AREA:1608 SQFT
BUILT-UP AREA:1406 SQFT**

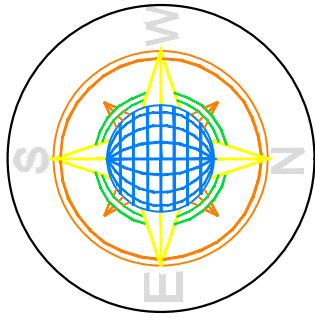

DRAWING TITLE: FIRST FLOOR PLAN

**DATE: 15-08-2026
SCALE: 1:100**

**DRAWN BY:
KISHOR KUMAR A,ARCHITECT/ENGINEER
BENGALURU**