


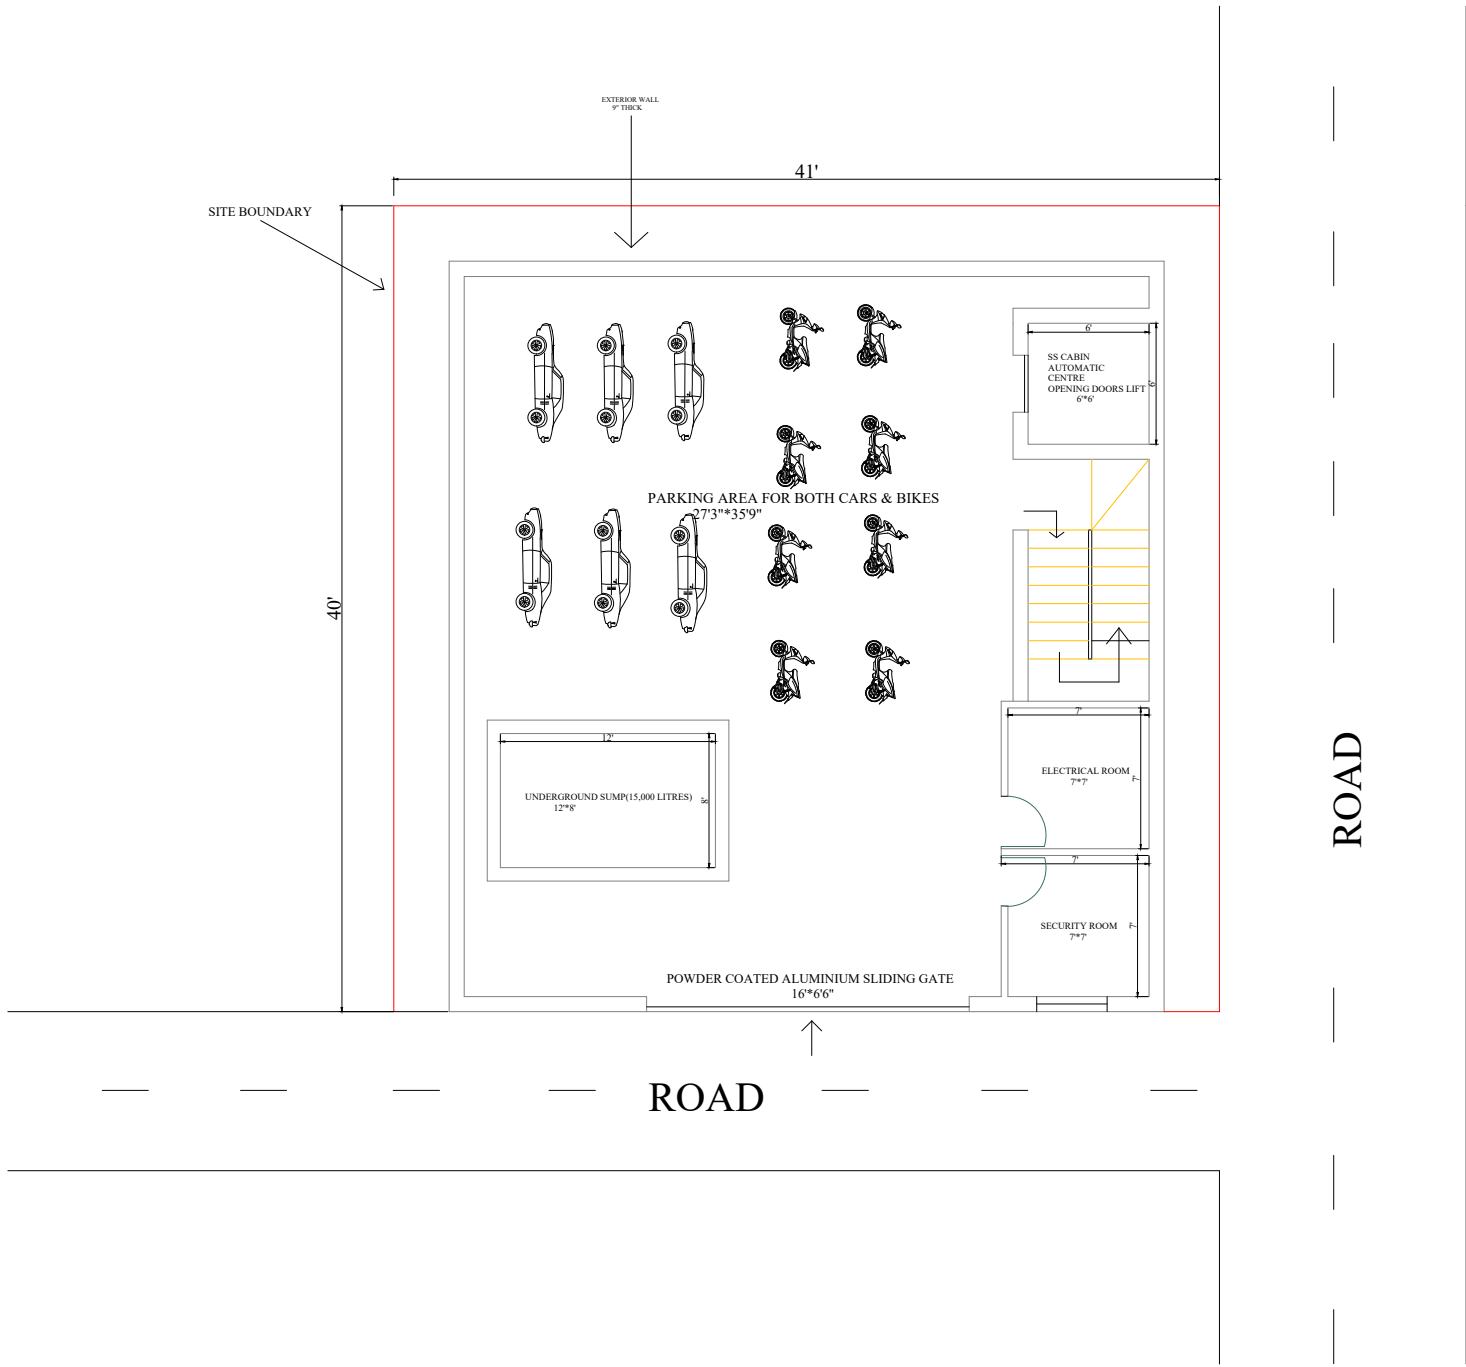


KEY NOTES:

- 1.SECURITY ROOM WALL=4" THICK
- 2.ELECTRICAL ROOM WALL=4" THICK
- 3.UNDERGROUND SUMP WALL(8" THICK)=15,000L-18,000L CAPACITY TOP SLAB=RCC ONE(150mm); COVER MATERIAL=MS FRAME+CHEQUERED PLATE
- 4.LIFT DOOR=SS 304 AUTOMATIC CENTRE OPENING with GRANITE FLOORING & CEILING-SS with LED LIGHTING HANDRAIL INSIDE LIFT-SS & MIRROR-FULL or HALF LIFT SHAFT WALL=9" THICK CAPACITY:544 KG MINIMUM 8 PEOPLES
- 5.BASEMENT FLOORING MATERIAL=TREMIX VACCUM DEWATERED CONCRETE(VDF) FLOORING(150mm thick) M:25 CONCRETE MIX
- 6.RCC DOG-LEGGED STAIRCASE TREAD=11";RISER=6";LANDING=6'*6';MATERIAL-20mm FLAMED GRANITE(anti-skid);SKIRTING=4"; HANDRAIL=SS 304,HEIGHT OF RAIL=3';GLASS RAILING (12mm TOUGHENED GLASS +SS 304) STAIR WALLS=9" BRICK MASONRY with SMOOTH PUTTY FINISH with PREMIUM PAINT FINISH
- 7.PARKING:6 CARS;12 BIKES
- 8.COMPOUND WALL=6";HEIGHT=7' MATERIAL:SOLID CEMENT BRICK or FLYASH BRICK MASONRY PLASTER:12mm ON BOTH SIDES & EXTERIOR WEATHER PROOF PAINT RCC COPING=3" THICK
- 9.MAIN ENTRANCE GATE:POWDER-COATED MS SLIDING GATE(SS 304 HARDWARE) with HEAVY DUTY ROLLERS & TRACKS

NOTE:ALL DIMENSIONS IN FEET & INCHES

CLIENT:
MR.IMRAN PASHA
PLACE:CHANDRA LAYOUT,BENGALURU

SITE AREA:1640 SQ FT
PLAN:GROUND FLOOR PLAN

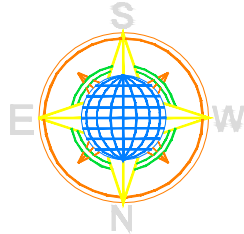

DRAWN BY:KISHOR KUMAR A
ARCHITECT/ENGINEER
BENGALURU